





# Anita Javadi

Creative and detail-oriented architect with 2 years of professional experience in residential design, façade development, and 3D modeling. Skilled in advanced architectural software, passionate about concept-driven design, and experienced in freelance and competition-based projects.



09198880245



anitaarchitect99@gmail.com

## Education

- 2019 – 2023 Bachelor's Degree in Architectural Engineering  
Islamic Azad University, South Tehran Branch

## Work Experience

- 2019 – 2020 Architectural Designer – Avang Sazan Co  
Designed phase 1 and phase 2 of residential buildings
- 2023 Created façade design for a hospital submitted to an architecture competition
- 2024 Led full design and 3D modeling of a café, including space planning and rendering
- 2022 – 2025 Completed multiple freelance architectural projects from concept to execution

# Skills

- Architectural detailing (Phase 1 & 2)
- Façade design and concept development
- High-quality rendering & visualization
- Interior and exterior spatial design

Skills



# 01



facade modeling

# 02



Girls' dormitory

# 03



Apadana Hospital

# 04



residential  
complex

# 05



Cafe design

# FACADE MODELING

 Tehran , ponak



# 01 FACADE MODELING





533  
Apartment





# Modern building facade

Modern facade design emphasizes clean lines, minimalism, and innovative use of materials. It blends aesthetics with functionality to create visually striking and efficient structures.

CONTACT

09198880245

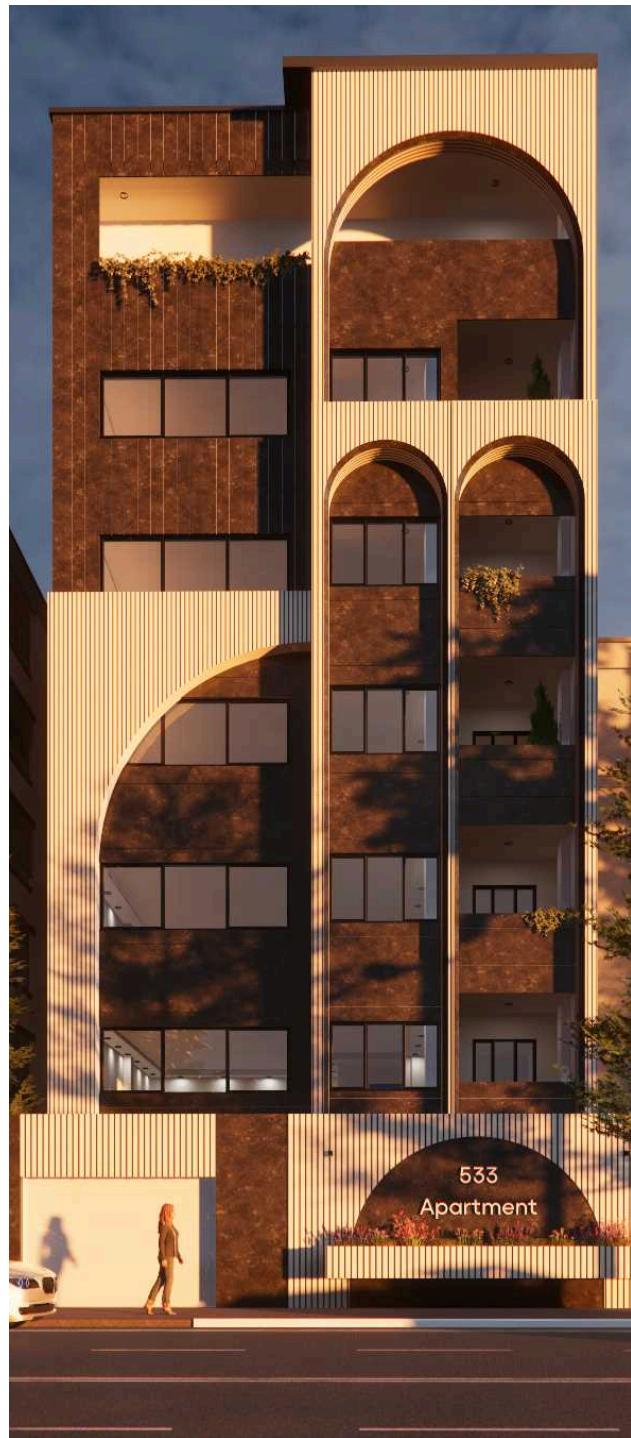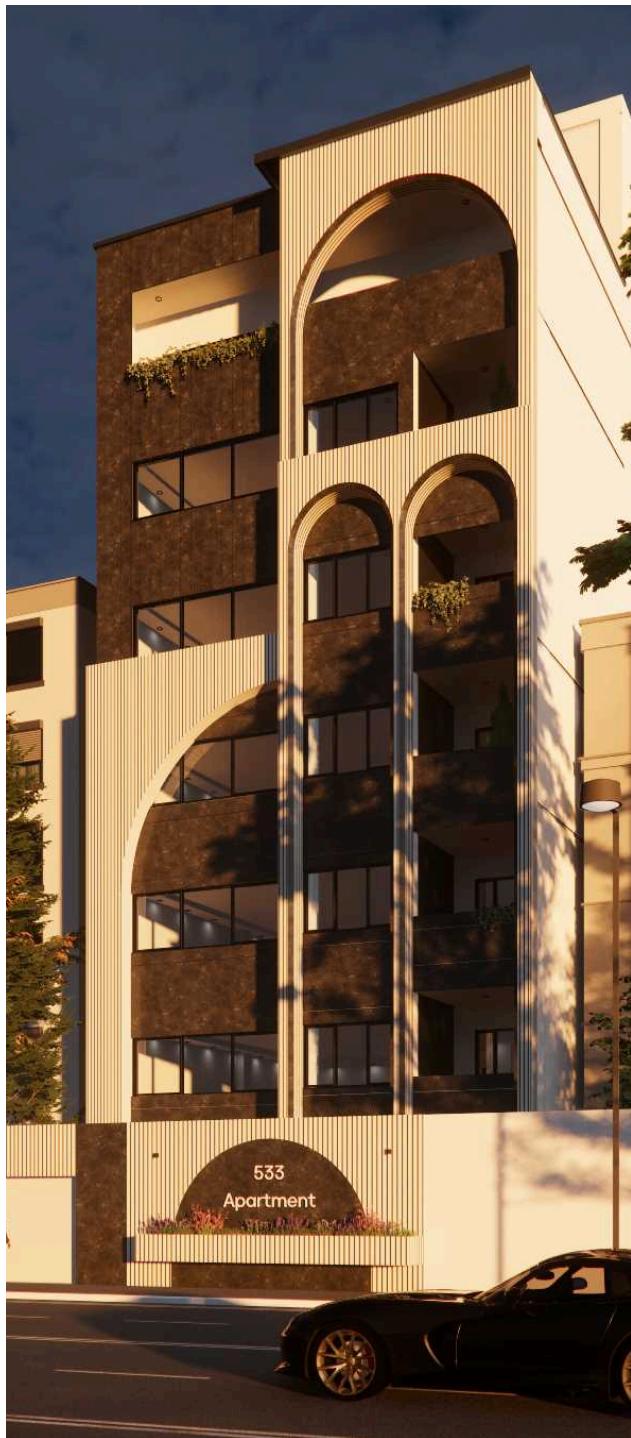


CONTACT

0919880245



# FACADE MODELING

facade modeling

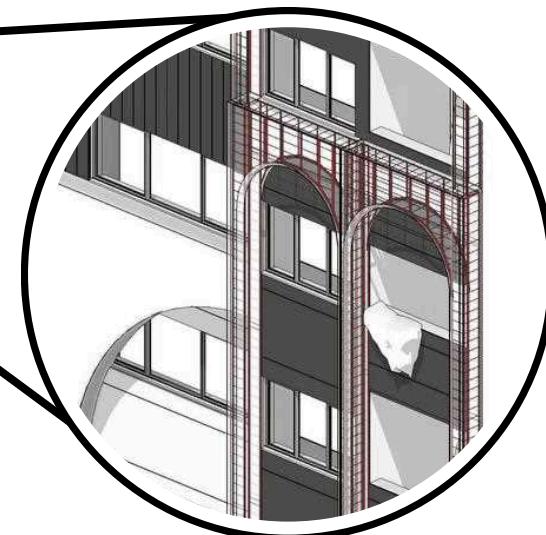


# material

USING THE LATEST MATERIAL



CONTACT

09198880245

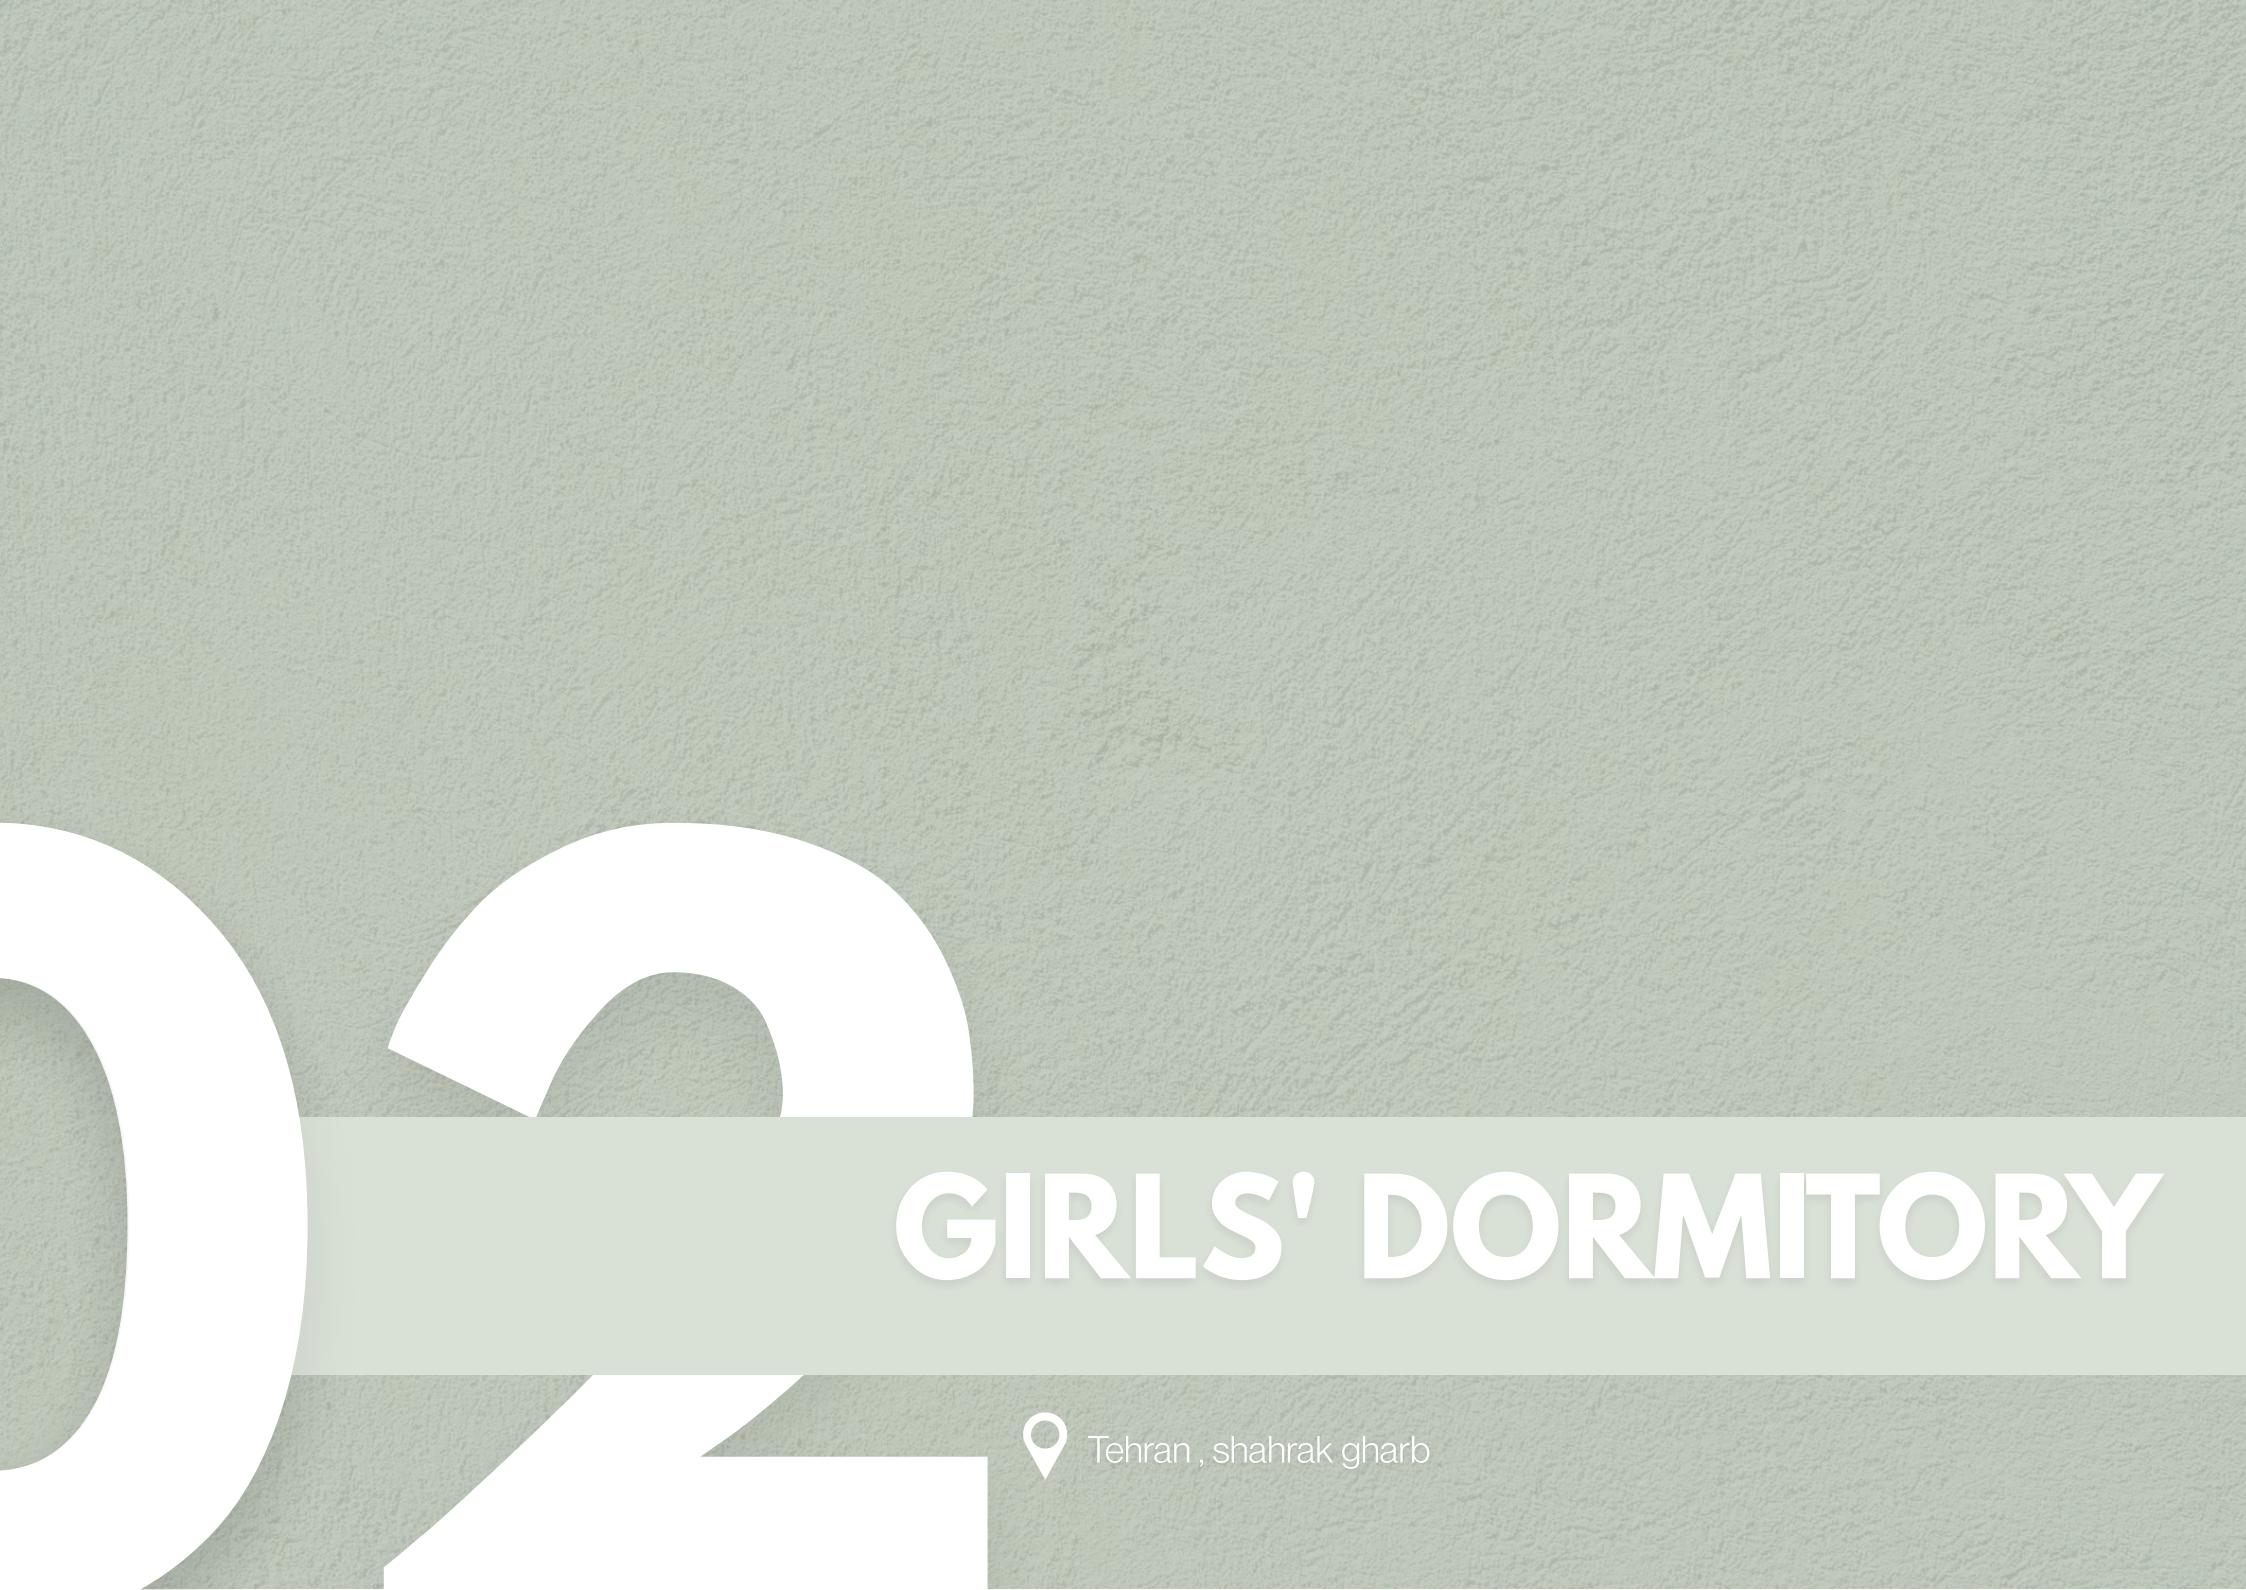

# GIRLS' DORMITORY



Tehran , shahrak gharb



02

## GIRLS' DORMITORY









# Diagram


Girls' dormitory

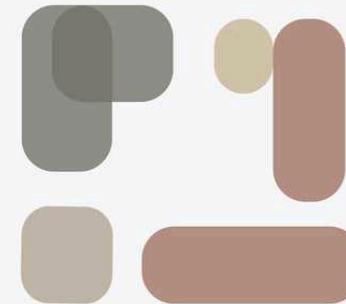


general  
administrative  
library

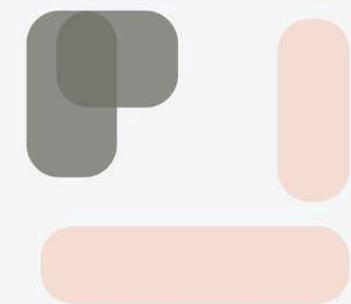

DORMITORY  
Service department

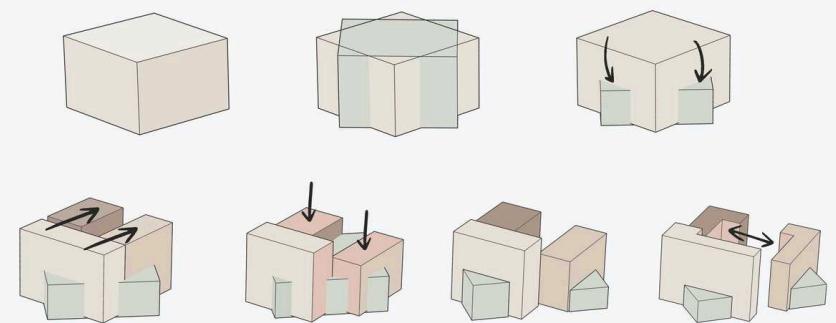

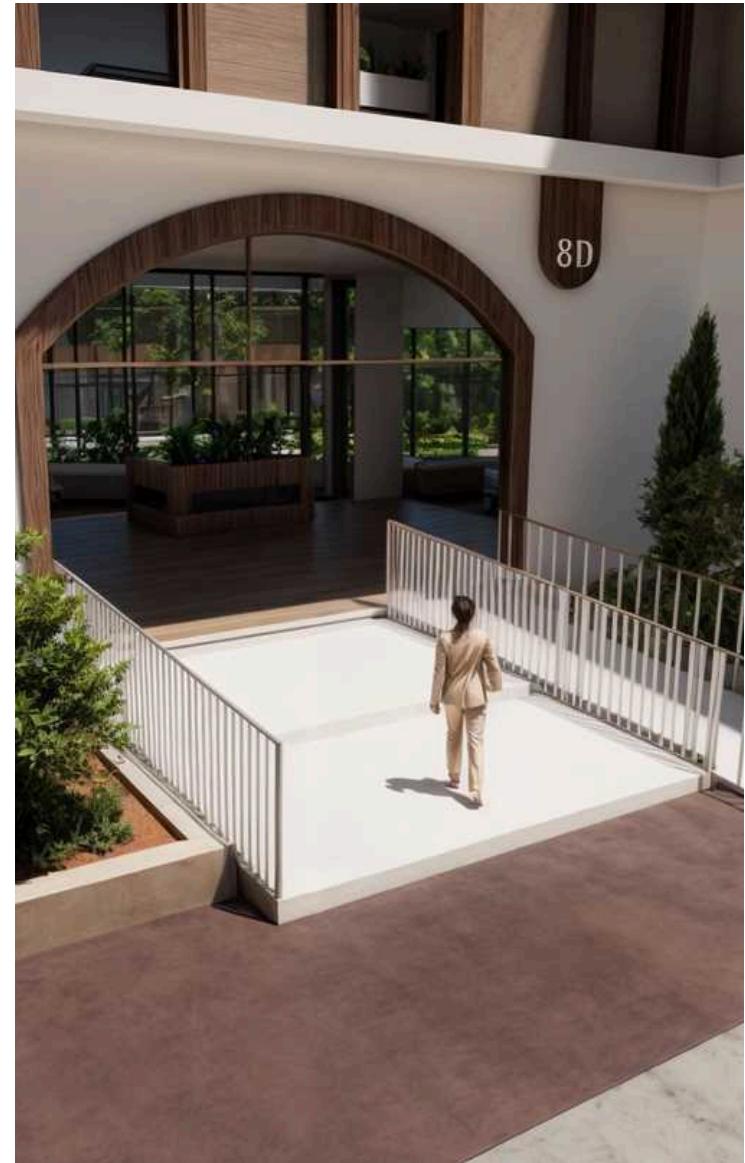

CONTACT

0919 888 0245



# Girls' dormitory design

Designing a girls' dormitory requires a focus on safety, privacy, and comfort. Secure entry points and surveillance systems are essential for protection. Private or semi-private rooms with adequate storage support personal space. Communal areas should encourage social interaction while maintaining a respectful environment.




# Girls' dormitory design


Designing a girls' dormitory today involves integrating smart technology for security and convenience. Spaces should promote well-being with natural lighting, ventilation, and calming interiors. Flexible study and relaxation zones support both academic focus and mental health. Sustainability and energy efficiency are also key considerations in modern dorm design.



# Dormitory entrance

The concept behind the entrance element is inspired by the overall form of a traditional home, designed to evoke a sense of invitation and belonging for the residents. This architectural gesture has been intentionally halved — one part referencing the memory of the original home, and the other symbolizing the beginning of a new chapter in the student's life. This duality creates a meaningful transition, blending familiarity with a sense of forward-looking identity in the new living environment.

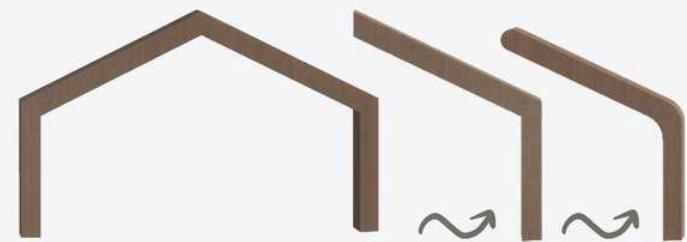

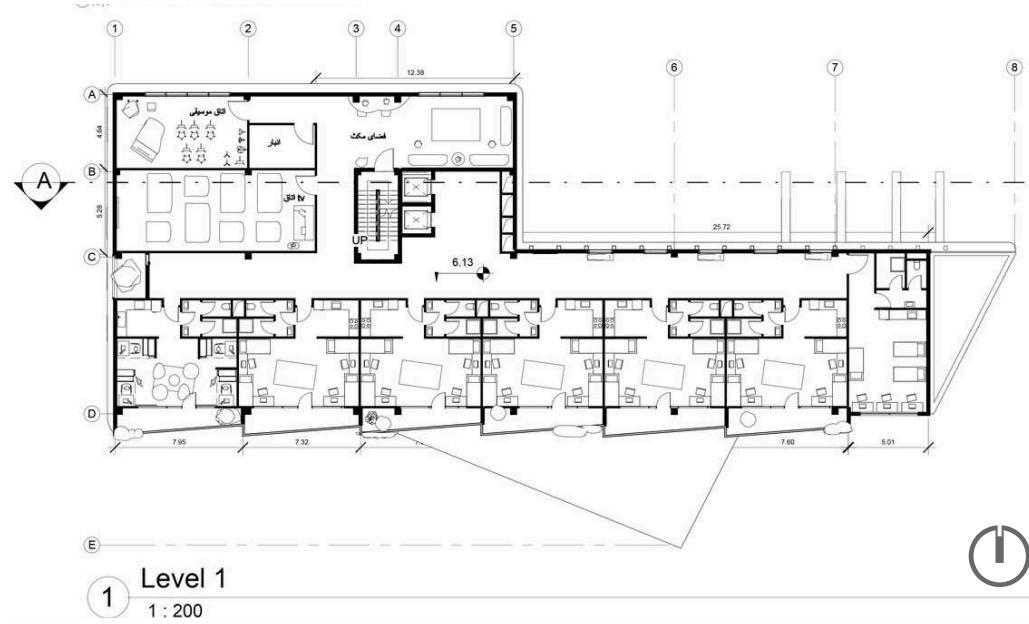


# Dormitory rooms


The room layouts have been meticulously designed with the highest level of sensitivity to ensure that female students experience maximum comfort and ease. Every spatial element has been carefully considered to eliminate potential challenges, creating a living environment that fully supports their daily routines, privacy, and well-being.



# section

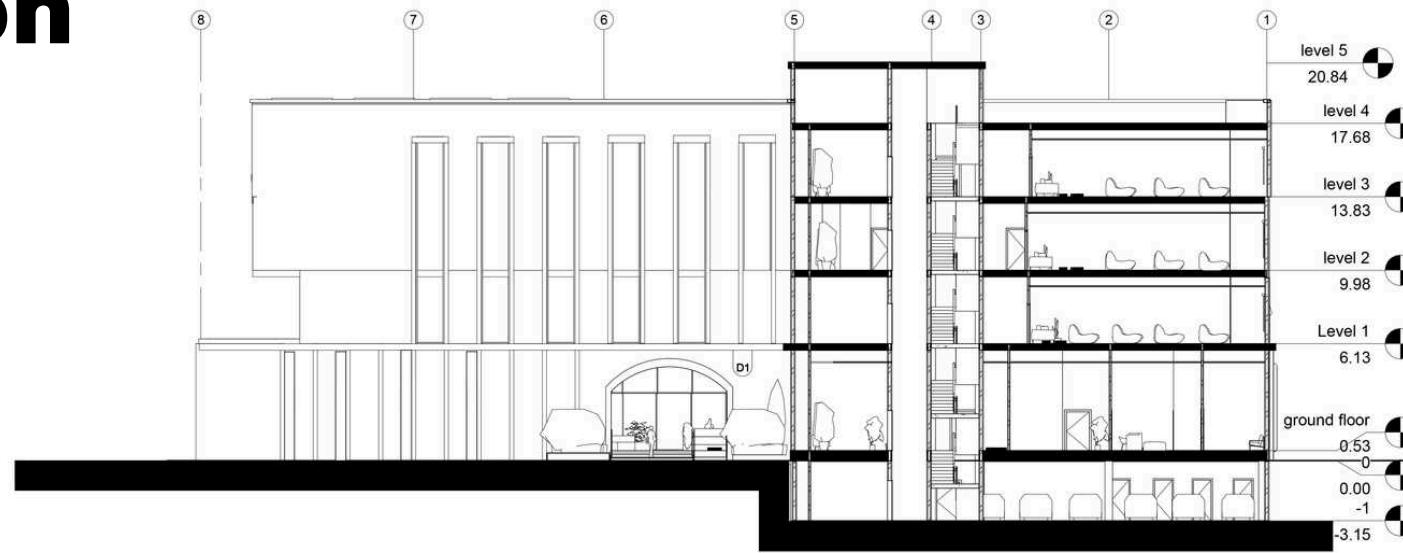


1 Section A-A  
1 : 200

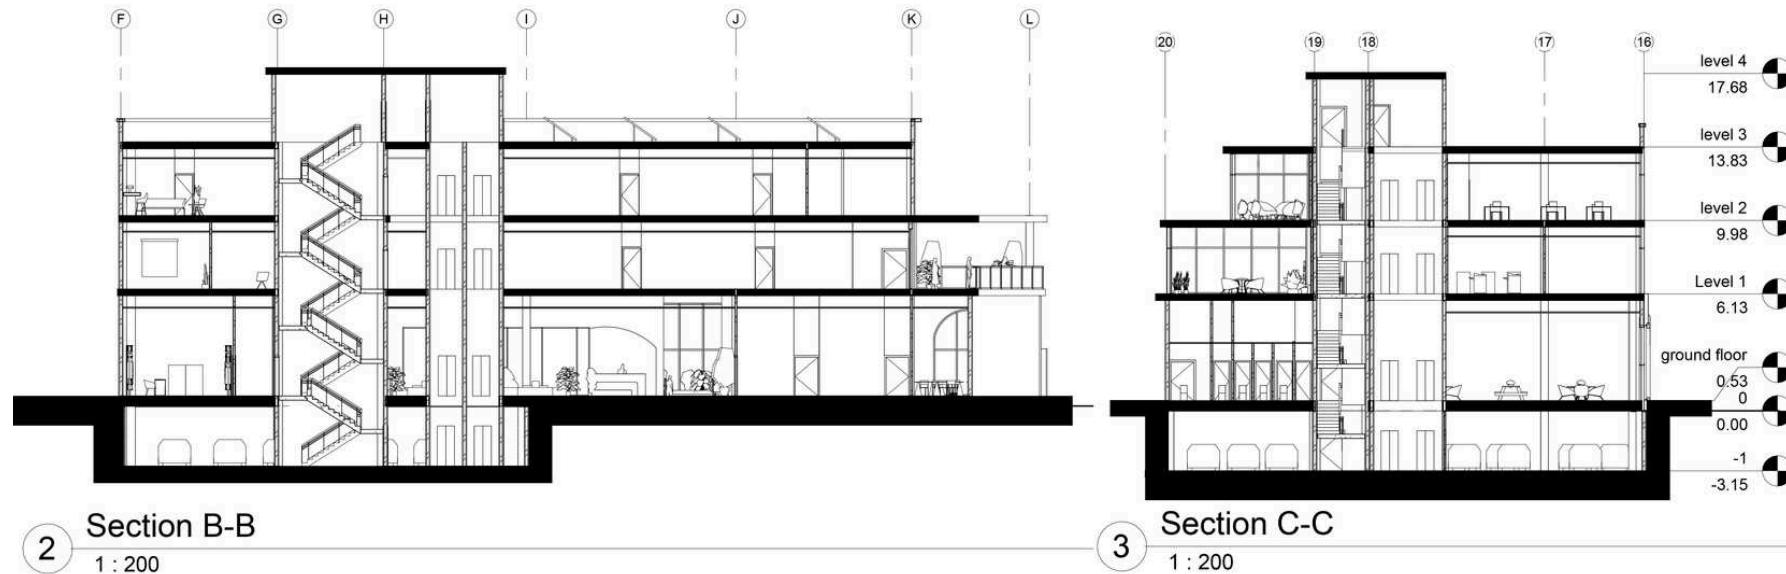

2 Section B-B  
1 : 200

3 Section C-C  
1 : 200

# facade

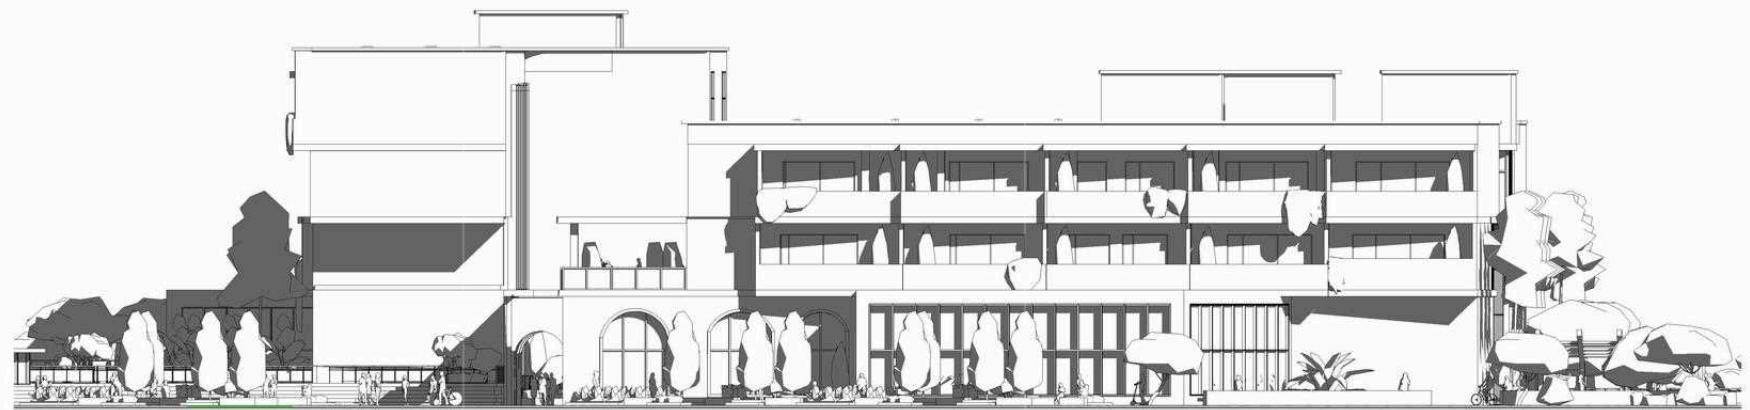

1 East  
1 : 200



2 West  
1 : 200

# APADANA HOSPITAL



Esfahan , sepahan shahr



03

## APADANA HOSPITAL



**ESPADANA**





# APADANA HOSPITAL

CONTACT

09198880245



# APADANA HOSPITAL

CONTACT


09198880245



CONTACT  
09198880245



CONTACT  
09198880245

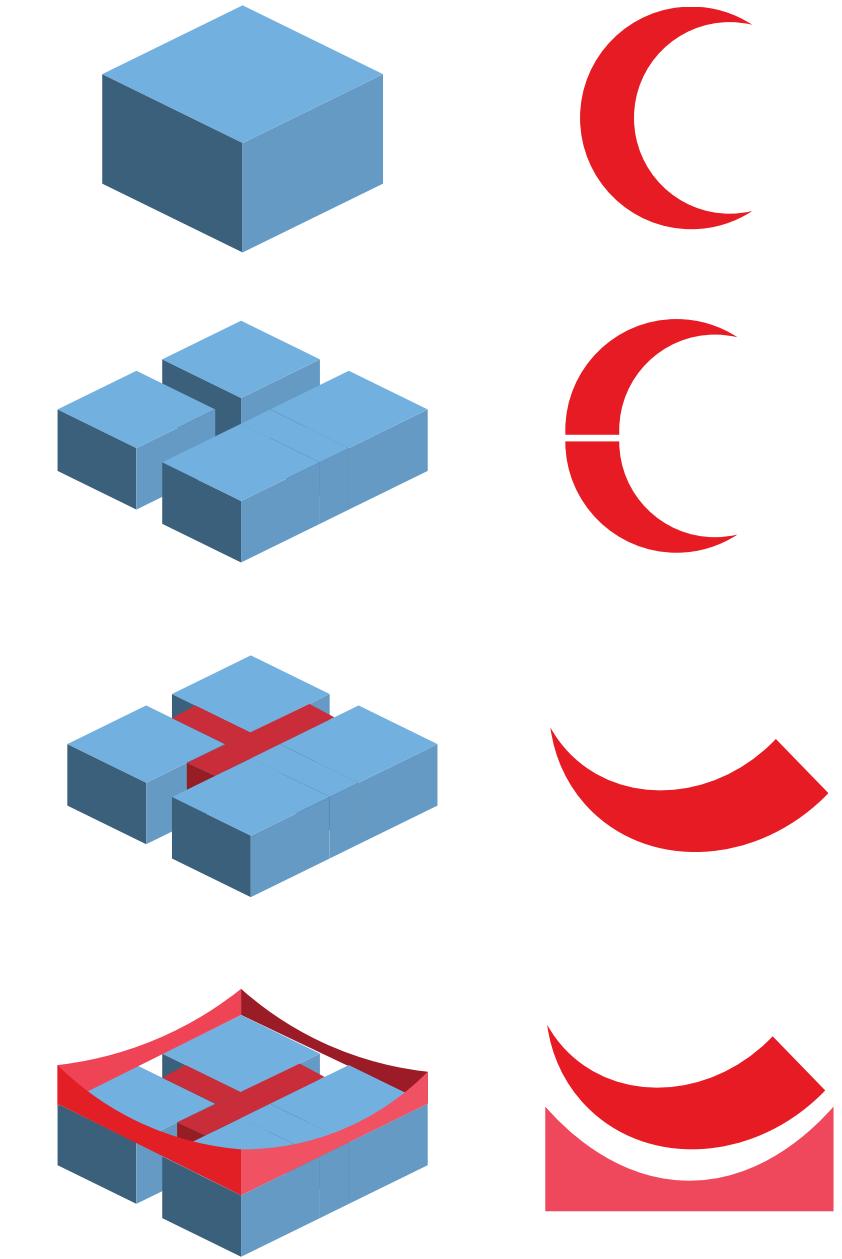

# RESIDENTIAL COMPLEX



Tehran, Sa'adat Abad



# 04 RESIDENTIAL COMPLEX







# residential complex

Designing a residential complex requires a balance of privacy, community, and functionality. Efficient space planning and natural light are essential for comfortable living. Public amenities like green spaces, playgrounds, and shared facilities enhance social interaction. Safety, accessibility, and sustainability must also be integrated into the overall design.

CONTACT

09198880245



CONTACT  
09198880245

# CAFE DESIGN



Tehran , Damavand

one more cup of coffee



## 05 CAFE DESIGN

one more cup of coffee



one more cup of coffee




one more cup of coffee






café

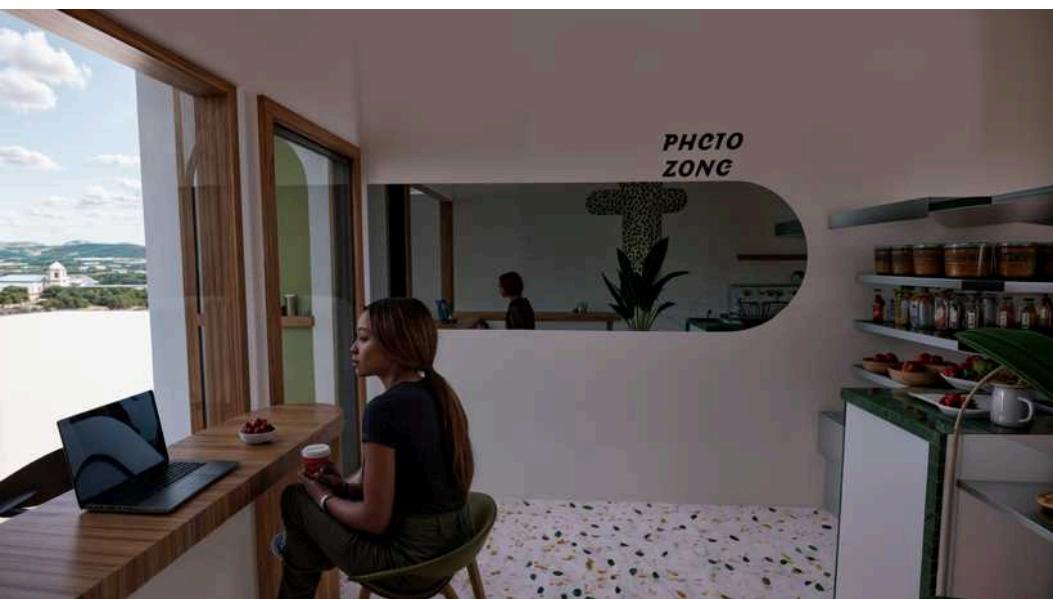





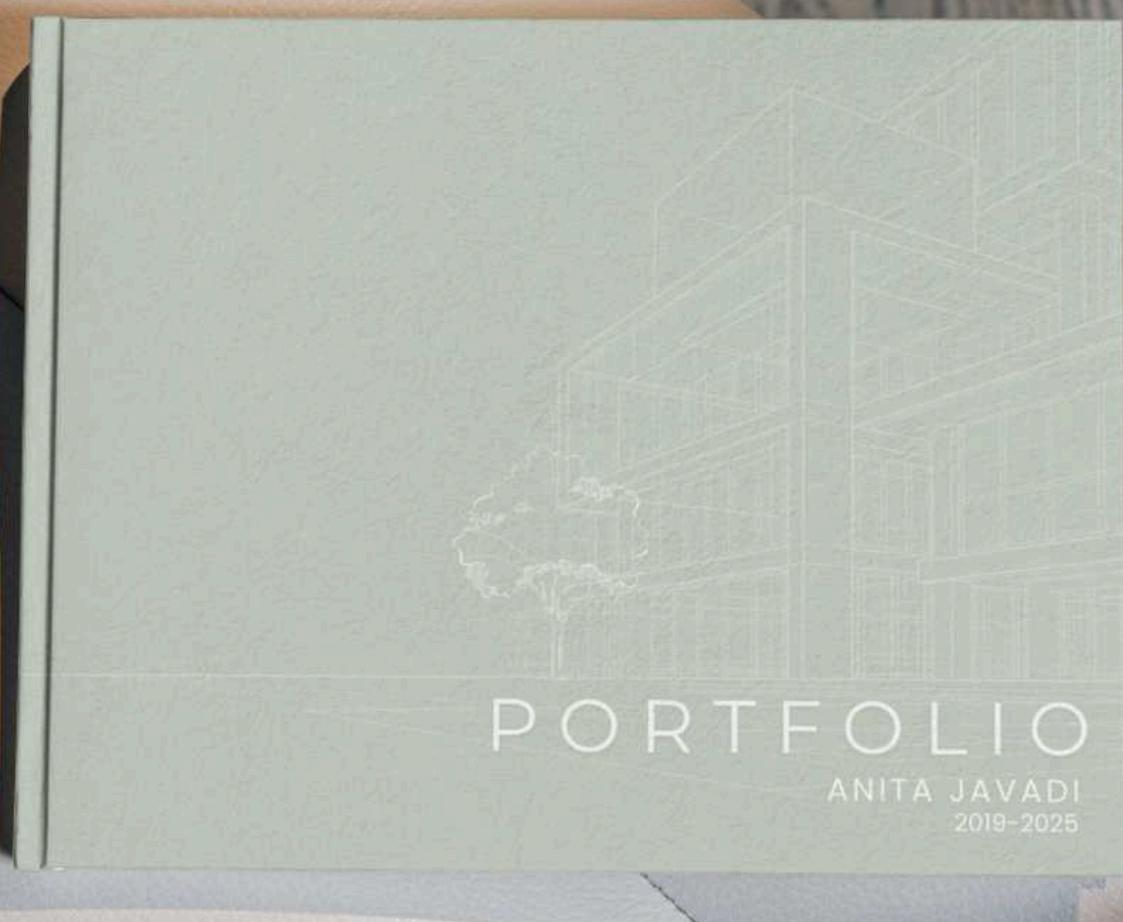

# PORTFOLIO

ANITA JAVADI  
2019-2025

